SUBMITTAL COVER

(Attach to each submittal)

21
Submittal No. Contractor only

Architect Project Number: 22-03

Contractors Number: 1

Project Name: Yorktown Highway Garage

Date returned:

Contractor: Peter A. Camilli & Sons Construction Ltd.
Address: 210 Marble Avenue – Pleasantville, New York 10570
Phone / Fax: 914-769-1164 – FAX – 914-741-6082

TYPE OF SUBMITTAL
(Check one)

- [X] Product Data
- [X] Shop Drawings
- [ ] Other
- [ ] Color Selection
- [ ] Sample
- [ ] O&M Manual
- [ ] Record Document

SUBSTITUTION
See General Conditions

[X] YES [ ] NO

DATE OF SUBMITTAL: 11-02-24

RESUBMITTED: 07-11-25

NUMBER OF ATTACHED: 1

PRODUCT IDENTIFICATION

Specification Section No.: Div 9 - Sec 5113 - Alum Windows
Contract Dwg. No.:
Product Name: Kawneer Alum Windows
Part/Paragraph:
Detail Reference:
Manufacturer: Same

CONTRACTOR APPROVAL

Identify that this submittal has been reviewed and approved by the Contractor in accordance with the General Conditions

By: BC Date: 7-11-2025

Deviation from Contract Documents:

Contractor Comments:

As per our telephone and email conversations - includes revised drawings including bathroom ext window openings

FOR USE BY CPL

SHOP DRAWING

No Exception Taken
Furnish as Corrected
Revise & Resubmit
Rejected

Corrections or comments made on the shop drawings during this review do not relieve the Contractor from compliance with the requirements of the drawings and specifications. This check is only for review of general conformance with the design concept of the project and general compliance with the information given in the contract documents. The Contractor is responsible for: confirming and correlating all quantities and dimensions; selecting fabrication processes and techniques of construction; coordinating his work with that of all other trades; and performing his work in a safe satisfactory manner.

Date: 07.21.25 By: David Tetro

Architect's Comments:

System to be Thermally Broken.

U-Values and R-Values to match those in the Specifications.

RECEIVED STAMP

RECEIVED
July 12, 2025
David A. Tetro
Architect P.C.

TOWN OF YORKTOWN
HIGHWAY GARAGE ADDITION & ALTERATION

ADDITION AND LEVEL-2 ALERATTION
281 UNDERHILL AVENUE-YORKTOWN HEIGHTS, NY 10598

GENERAL CONTRACTOR:
PETER A. CAMILLI & SONS CONSTRUCTION LTD.
210 MARBLE AVENUE
PLEASNTVILLE, NY 10570

ARCHITECH:
DAVID A. TETRO
302 LEWIS AVENUE
YORKTOWN HEIGHTS, NY 10598

SUB-CONTRACTOR:
TRIPLE C GLASS CORP. d/b/a MONSEY GLASS CONTRACTING
33 ROUTE 304
NANUET, NY 10954

SHOP DRAWING FOR KAWNEER 451T-CG/ GLASSvent PROJECT OUT WINDOWS WITH 1/4" GRAY TEMPERED GLASS OVER TEMPERED SOLARBAN 70 LOW-E GLASS. 1" THICK OVERALL INSULATED GLASS.

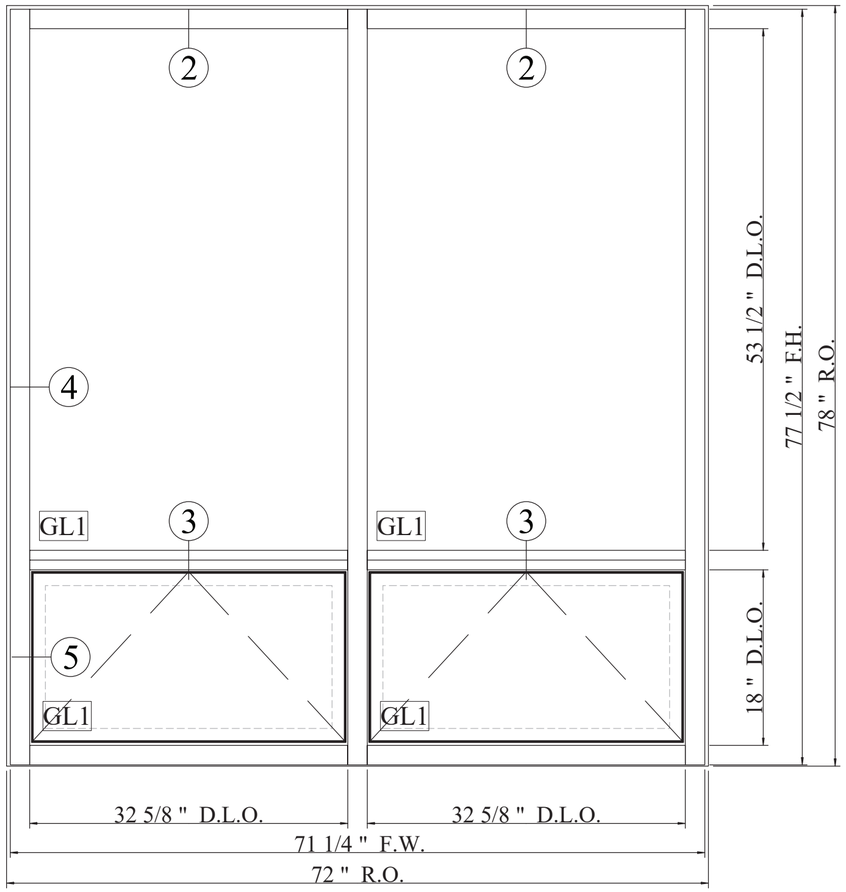

BUNK ROOM WINDOWS (3-OPENINGS)
SCALE: 3/4" = 1'-0"

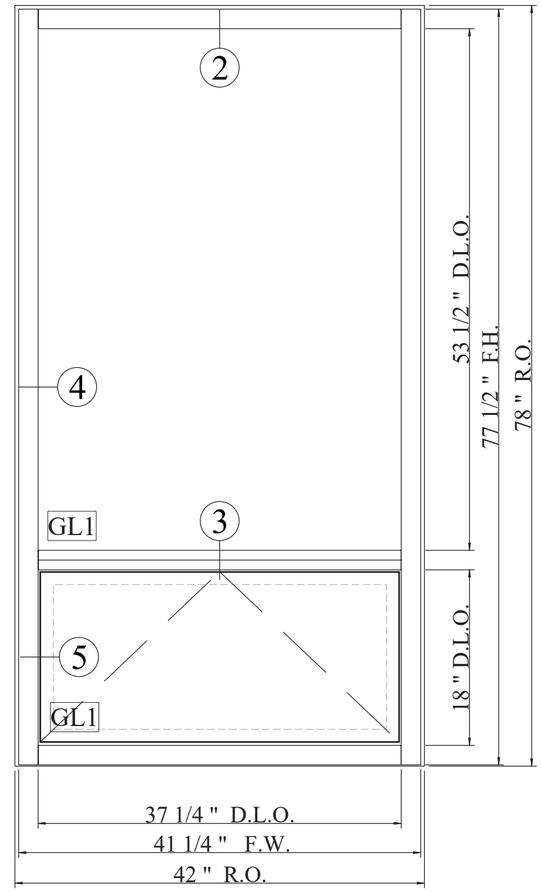

SUPERINTENDANTS OFFICE (2 OPENINGS)
SCALE: 3/4" = 1'-0"

GL1 = 1/4" TEMPERED GRAY/ SOLAR BAN 70 LOW-E CLEAR

GL2 = 1/4" TEMPERED GRAY/ FROSTED ACID ETCHED GLASS

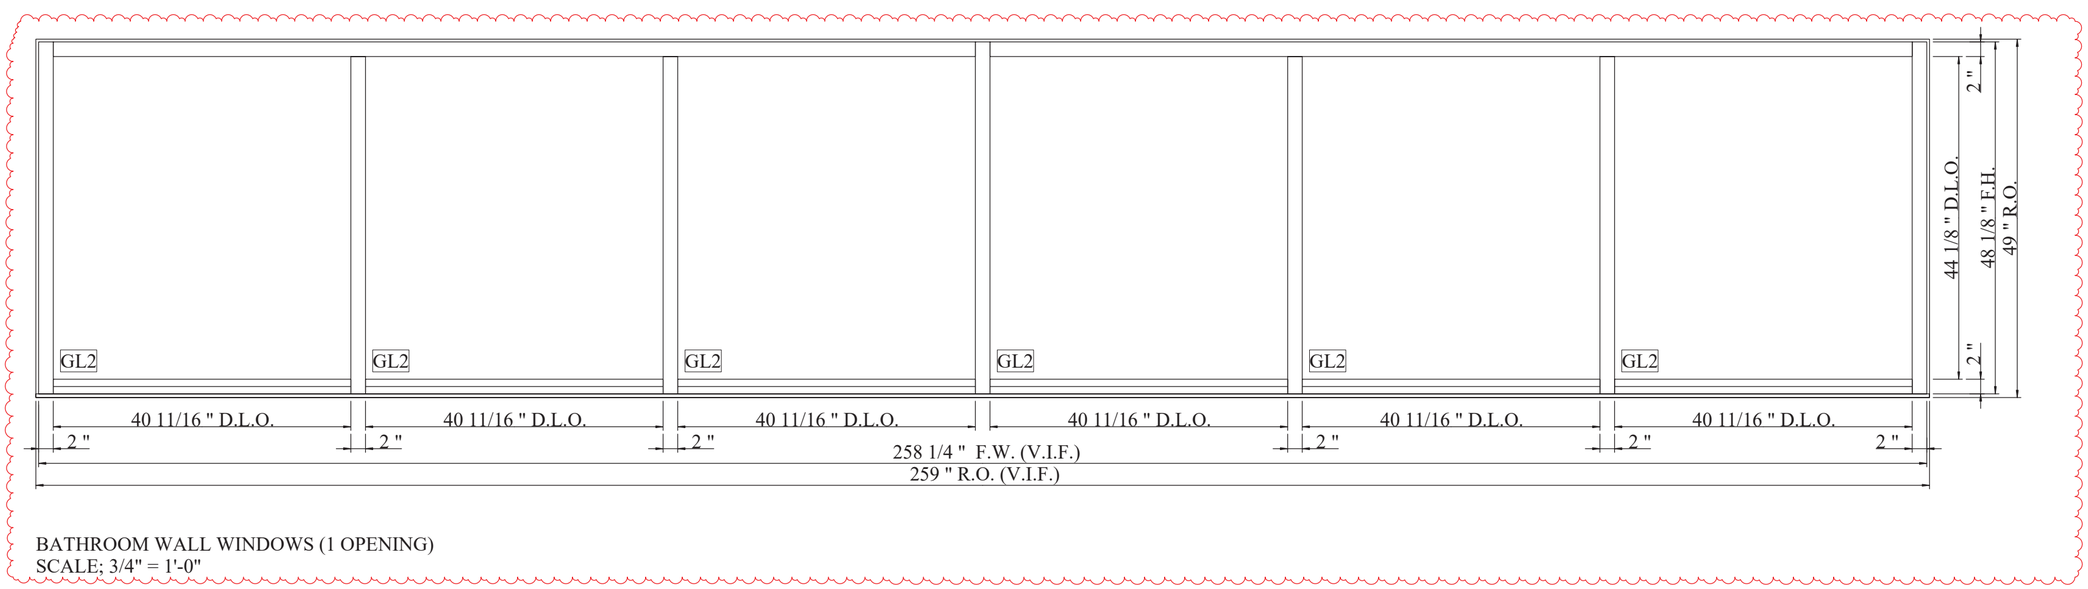

BATHROOM WALL WINDOWS (1 OPENING)
SCALE; 3/4" = 1'-0"

MONSEY GLASS CONTRACTING CO.	CONTRACTOR: PETER A. CAMILLI & SONS CONSTRUCTION LTD.	ARCHITECH: DAVID A. TETRO	MANUFACTURE: KAWNEER	SCALE: AS NOTED	TITLE:	PAGE:
	JOB NAME: YORKTOWN HIGHWAY GARAGE	OWNER: TOWN of YORKTOWN	PRODUCT: 451T CENTER SET W/ GLASSvent PROJECT OUT WINDOW	DRAWN BY: CHARLIE SQUILLANTE JR.	WINDOW ELEVATIONS	SD01
	JOB LOCATION: 281 UNDERHILL AVENUE, YORKTOWN HEIGHTS	DATE DRAWN: 10/29/2024	COLOR: CLASS II #40 BRONZE ANODIZED.			
		REVISION DATE(S): 07/09/2025	GLASS TYPE: 1"o.a TEMPERED GRAY OVER SOLARBAN 70 LOW-E IG			

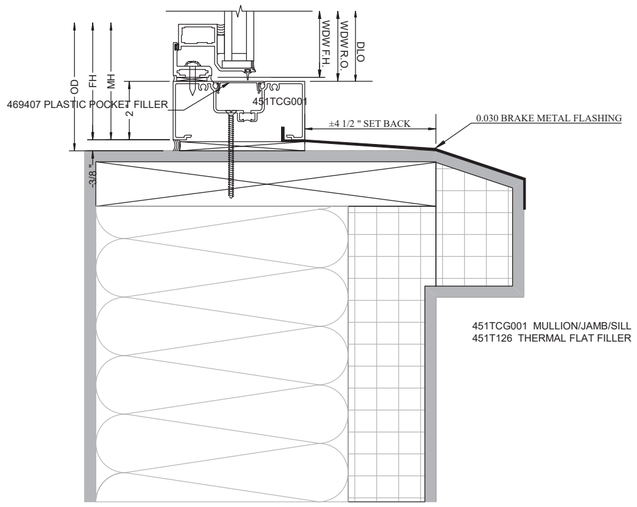

① WINDOW SILL DETAIL TYP.
SCALE: 1 1/2" = 1'-0"

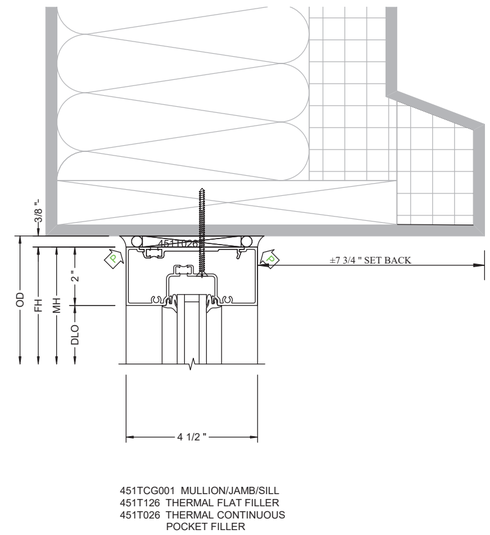

② FIXED WINDOW HEAD DETAIL TYP.
SCALE: 1 1/2" = 1'-0"

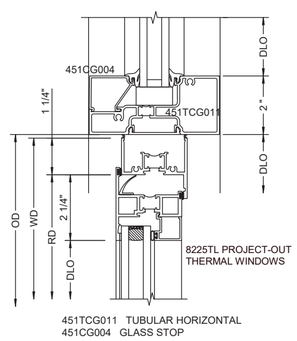

③ WINDOW JOINING DETAIL TYP.
SCALE; 1 1/2" = 1'-0"

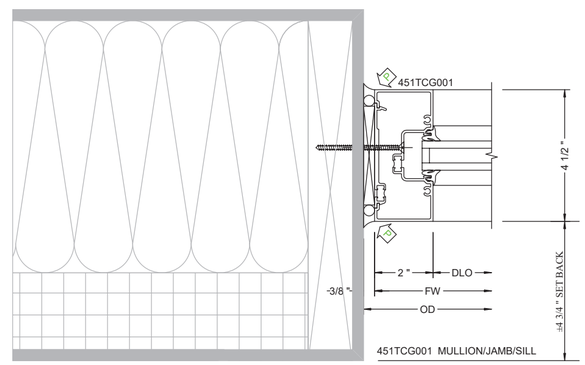

④ WINDOW JAMB DETAIL TYP.
SCALE; 1 1/2" = 1'-0"

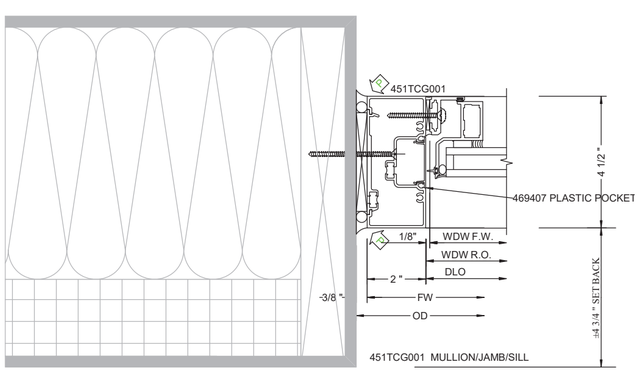

⑤ WINDOW JAMB DETAIL TYP.
SCALE; 1 1/2" = 1'-0"

MONSEY GLASS CONTRACTING CO.	CONTRACTOR: PETER A. CAMILLI & SONS CONSTRUCTION LTD.	ARCHITECH: DAVID A. TETRO	MANUFACTURE: KAWNEER	SCALE:	TITLE:	PAGE:
	JOB NAME: YORKTOWN HIGHWAY GARAGE	OWNER: TOWN of YORKTOWN	PRODUCT: 451T CENTER SET W/ GLASSvent PROJECT OUT WINDOW	DRAWN BY: CHARLIE SQUILLANTE JR.	WINDOW DETAILS	SD01
	JOB LOCATION: 281 UNDERHILL AVENUE, YORKTOWN HEIGHTS	DATE DRAWN: 10/29/2024	COLOR: CLASS II #40 BRONZE ANODIZED.			
		REVISION DATE(S): 07/09/2025	GLASS TYPE: 1"o.a TEMPERED GRAY OVER SOLARBAN 70 LOW-E IG			

Features

- Trifab® VersaGlaze® 451/451T is 4-1/2" (114.3) deep with a 2" (50.8) sightline
- ~~Front~~, Center, Back ~~or Multi-Plane glass applications~~
- Flush glazed from either the inside or outside
- Screw Spline, ~~Shear Block, Stick or Continuous Head and Sill fabrication~~
- ~~Screw Spline Pre-Glazed option~~
- ~~SSG / Weatherseal option~~
- IsoLock® lanced and debridged thermal break option with Trifab® VersaGlaze® 451T
- ~~Infill options up to 1-1/8" (28.6) thickness~~
- Permanodic® anodized finishes option
- ~~Painted finishes in standard and custom choices~~

Optional Features

- Acoustical rating per AAMA 1801 and ASTM E 1425
- Project specific U-factors (See Thermal Charts)
- Integrates with Versoleil® SunShade Outrigger System and Horizontal Single Blade System
- Profit$Maker® Plus die sets available

Product Applications

- Storefront, Ribbon Window, Punched Openings ~~or Pre-Glazed~~
- Single-span
- ~~Integrated entrance framing allowing Kawneer standard entrances or other specialty entrances to be incorporated~~
- Kawneer windows or GLASSvent® Windows for Storefront Framing are easily incorporated

Laws and building and safety codes governing the design and use of Kawneer products, such as glazed entrance, window, and curtain wall products, vary widely. Kawneer does not control the selection of product configurations, operating hardware, or glazing materials, and assumes no responsibility therefor.

Kawneer reserves the right to change configuration without prior notice when deemed necessary for product improvement.

© 2018, Kawneer Company, Inc.

For specific product applications,
consult your Kawneer representative.

The split vertical in the **Screw Spline** system allows a frame to be installed from unitized assemblies. Screws are driven through the back of the verticals into splines extruded in the horizontal framing members. The Individual units are then snapped together to form a complete frame.

SCREW SPLINE ASSEMBLY

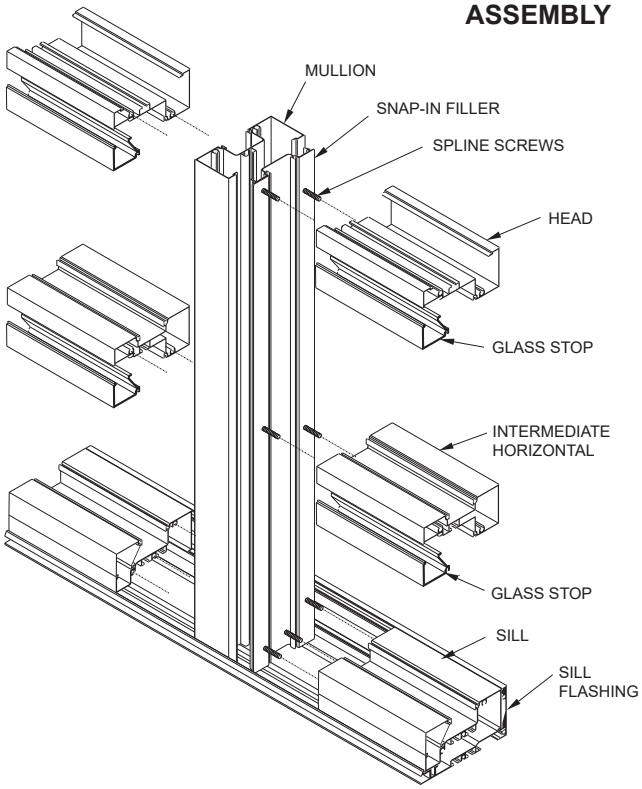

The **Shear Block** system of fabrication allows a frame to be pre-assembled as a single unit. Horizontals are attached to the verticals with shear blocks.

SHEAR BLOCK ASSEMBLY

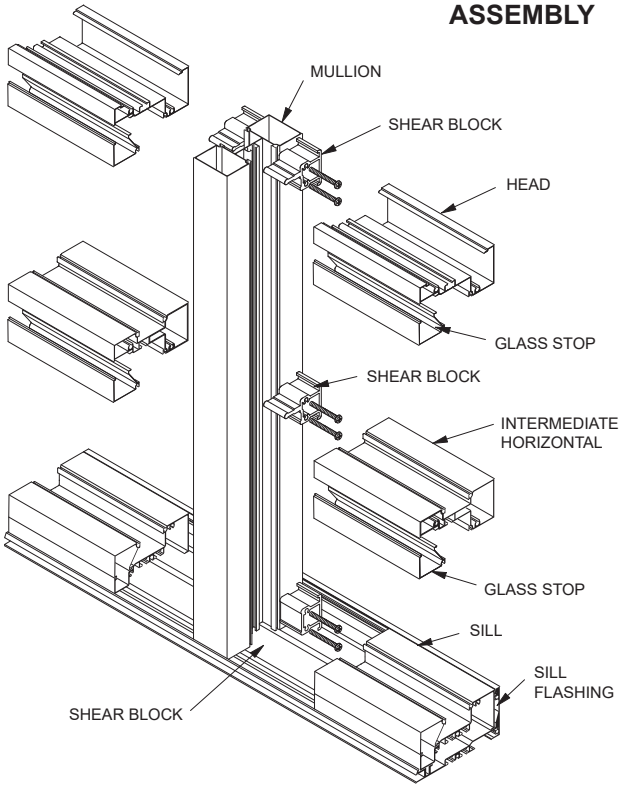

STICK ASSEMBLY

The **Stick** system allows on-site construction. Head and sill receptors are fastened to the surround. Vertical mullions are then installed in these receptors and are held in place by snap-in inserts. Intermediate horizontal members are attached to the verticals with shear blocks. Flashing is not required.

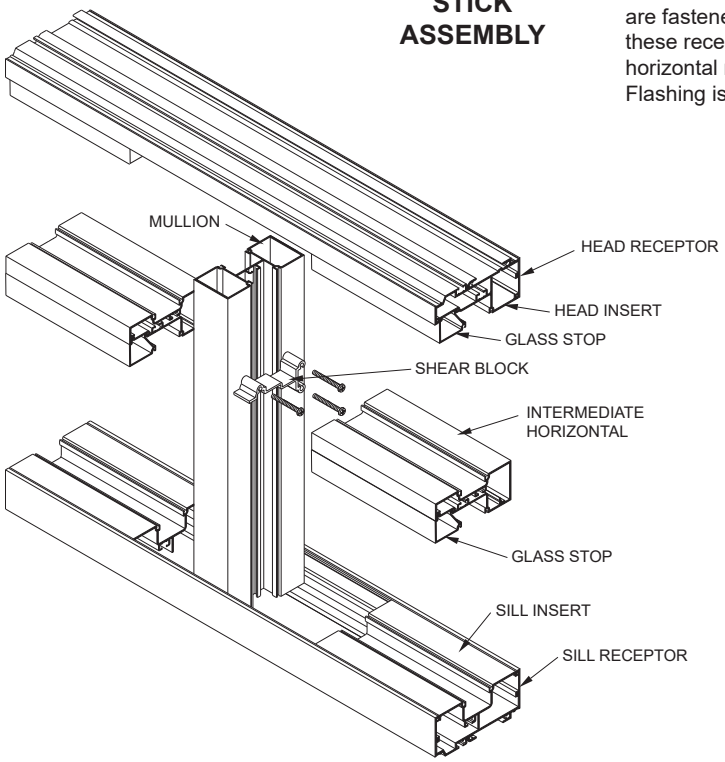

NOTE:
If the end reaction of the mullion (mullion spacing (ft.) times height (ft.) times specified wind load (psf) divided by two) is more than 500 lbs., the optional mullion anchors must be used. (See page 18)

Laws and building and safety codes governing the design and use of Kawneer products, such as glazed entrance, window, and curtain wall products, vary widely. Kawneer does not control the selection of product configurations, operating hardware, or glazing materials, and assumes no responsibility therefor.

Kawneer reserves the right to change configuration without prior notice when deemed necessary for product improvement.

© 2018, Kawneer Company, Inc.

Trifab® VersaGlaze® 451/451T Framing System

APRIL, 2024

BASIC FRAMING DETAILS (CENTER - Outside Glazed - Stops Up)

EC 97911-316

Additional information and CAD details are available at www.kawneer.com

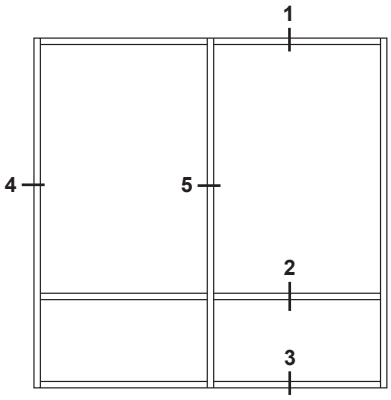

ELEVATION IS NUMBER KEYED TO DETAILS

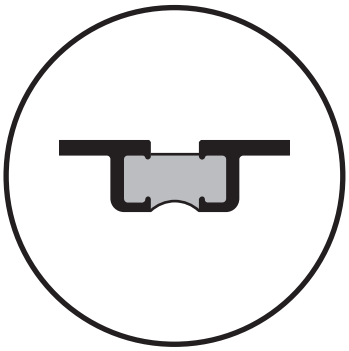

NUMBERS IN BRACKETS ARE THERMALLY BROKEN MEMBERS

SCREW SPLINE

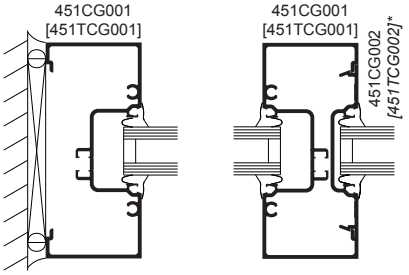

4 JAMB **5 VERTICAL**

1 HEAD

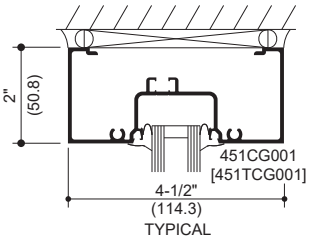

2 HORIZONTAL

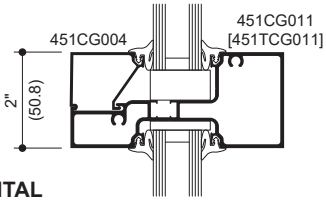

3 SILL

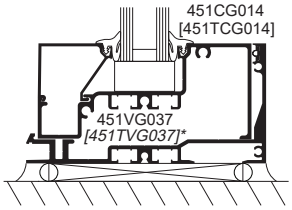

* HP Sill Flashing shown with optional gasket.

SHEAR BLOCK

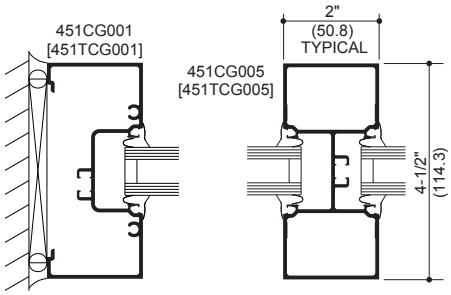

4 JAMB **5 VERTICAL**

1 HEAD

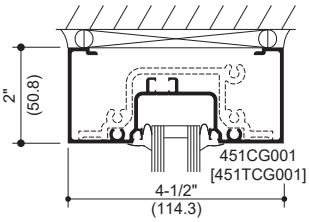

2 HORIZONTAL

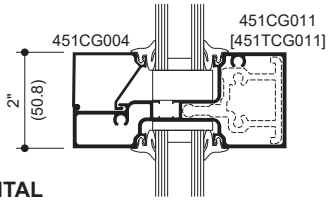

3 SILL

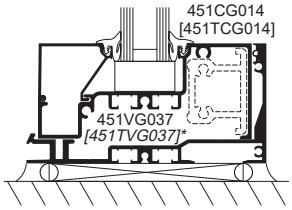

* HP Sill Flashing shown with optional gasket.

STICK

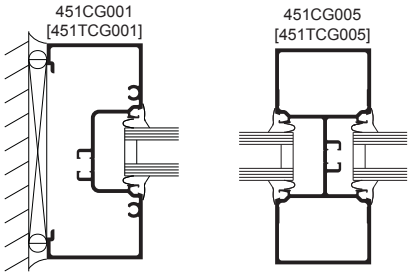

4 JAMB **5 VERTICAL**

1 HEAD

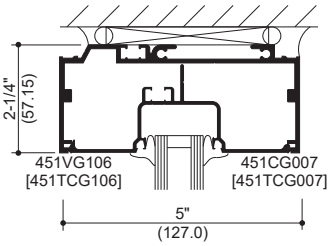

2 HORIZONTAL

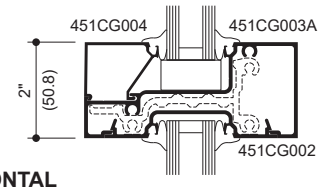

3 SILL

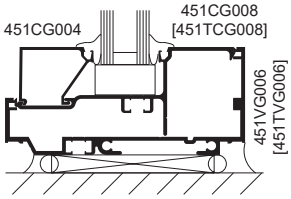

Laws and building and safety codes governing the design and use of Kawneer products, such as glazed entrance, window, and curtain wall products, vary widely. Kawneer does not control the selection of product configurations, operating hardware, or glazing materials, and assumes no responsibility therefor.

Kawneer reserves the right to change configuration without prior notice when deemed necessary for product improvement.

© 2018, Kawneer Company, Inc.

Additional information and CAD details are available at www.kawneer.com

PRE-GLAZED EXPANSION MULLIONS

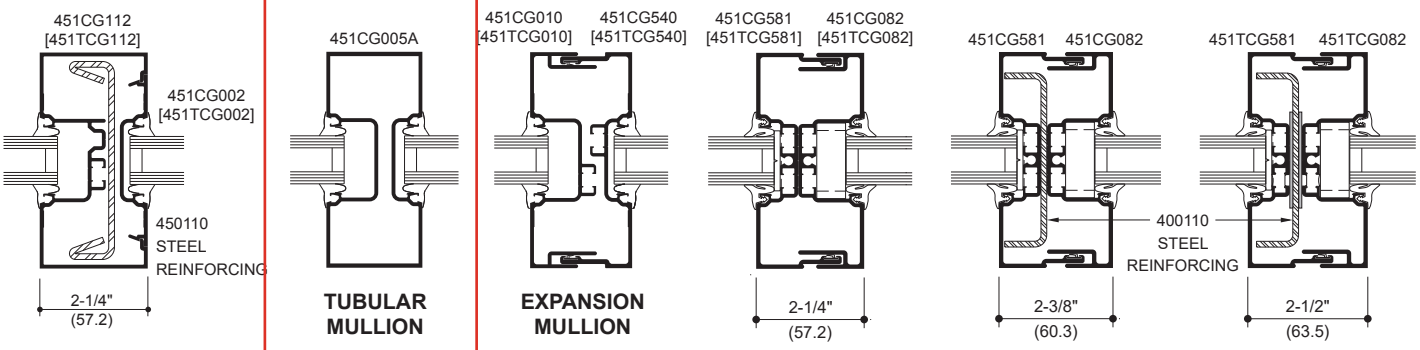

SPLIT MULLION W/ STEEL | **TUBULAR MULLION** | **EXPANSION MULLION** | **451/451T** | **451 W/ STEEL** | **451T W/ STEEL**

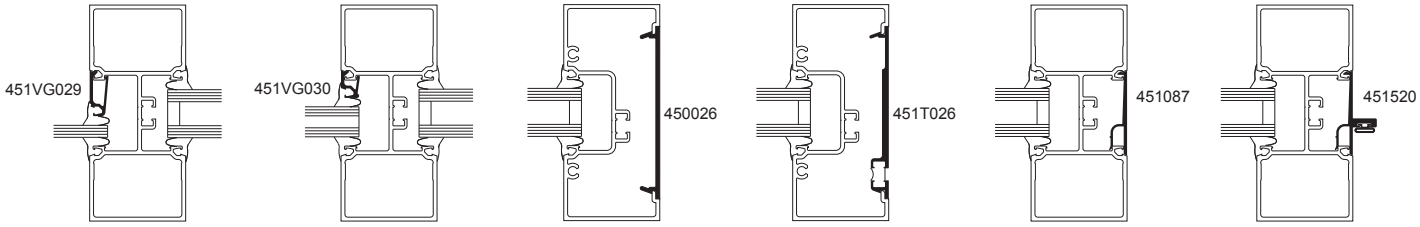

1/4" (6.4) INFILL SNAP-IN ADAPTOR | **5/8" (15.9) INFILL SNAP-IN ADAPTOR** | **SNAP-IN FLAT FILLER** | **THERMAL FLAT FILLER** | **SNAP-IN FLAT POCKET FILLER** | **SNAP-IN DOOR STOP**

SHALLOW POCKET | DEEP POCKET

THERMAL POCKET FILLERS

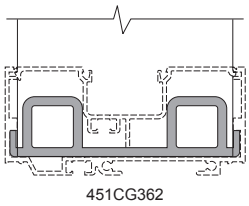

MULLION ANCHOR

NOTE:
If the end reaction of the mullion (mullion spacing (ft.) times height (ft) times specified wind load (psf), divided by two) is more than 500 LBS., the optional mullion anchor must be used. Consult Application Engineering.

NOTE:
Mullion Anchor not used with Lightweight Receptor.

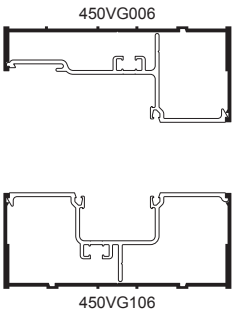

OPTIONAL LIGHTWEIGHT CAN RECEPTORS

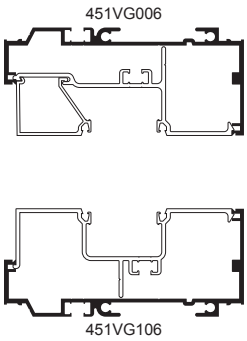

OPTIONAL UNEQUAL LEG CAN RECEPTORS

Laws and building and safety codes governing the design and use of Kawneer products, such as glazed entrance, window, and curtain wall products, vary widely. Kawneer does not control the selection of product configurations, operating hardware, or glazing materials, and assumes no responsibility therefor.

Kawneer reserves the right to change configuration without prior notice when deemed necessary for product improvement.

© 2018, Kawneer Company, Inc.

CLASS and GRADE	Heavy Commercial Grade P-HC40 – P-HC70
TESTING STANDARD	AAMA / WDMA / CSA / 101 / I.S.2 / A440 (NAFS)
SYSTEM DEPTH	2-3/4" Overall System Depth (1" Infill) 2-1/8" Overall System Depth (1/4" Infill)
TYPICAL WALL THICKNESS	0.090 Nominal Frame
TYPICAL MAX. VENT SIZE	60" x 36"
TYPICAL MIN. VENT SIZE	14" x 14"
INFILL OPTIONS	1" and 1/4"
STANDARD HARDWARE	Stainless Steel 4-Bar Hinges Cast White Bronze Cam Lock
OPTIONAL HARDWARE	Cam Lock with Pole Ring Sash Pole Pole Ring Access Control Lock Pivot-Shoe Roto-Operator (Verify with application engineering project specific limit stop requirements based on window size) Concealed Lock with removable key Hook Bolt Lock Limit Stop (Verify with application engineering project specific limit stop requirements based on window size)
OTHER OPTIONS	Insect Screens

Laws and building and safety codes governing the design and use of Kawneer products, such as glazed entrance, window, and curtain wall products, vary widely. Kawneer does not control the selection of product configurations, operating hardware, or glazing materials, and assumes no responsibility therefor.

Kawneer reserves the right to change configuration without prior notice when deemed necessary for product improvement.

© 2015, Kawneer Company, Inc.

GLASSvent® Windows for Storefront Framing

Additional information and CAD details are available at www.kawneer.com

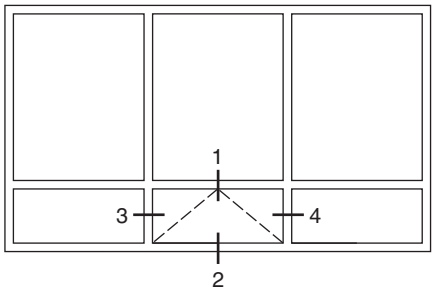

ELEVATION IS NUMBER KEYED TO DETAILS

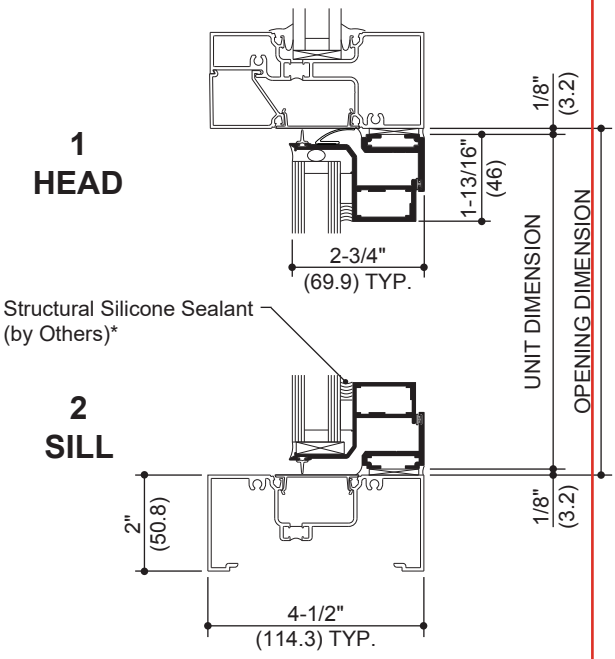

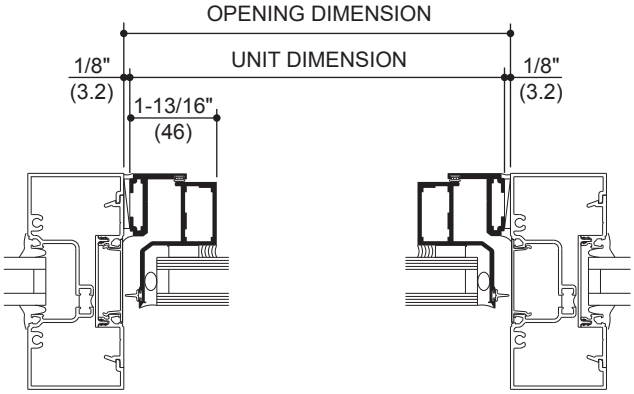

3
JAMB

4
JAMB

NOTE: THE KAWNEER GLASSvent® WINDOW IS SHOWN IN THESE DETAILS WITH TRIFAB® VERSAGLAZE® 451T STOREFRONT FRAMING FOR REFERENCE. OTHER KAWNEER SYSTEMS CAN BE USED. FOR PRODUCT SPECIFIC APPLICATIONS CONSULT YOUR KAWNEER REPRESENTATIVE.

*** INSTALLER NOTE:** Installer is responsible for all required compatibility review and approvals with the Structural Silicone Manufacturer and the Insulating Glass Unit Manufacturer.

Laws and building and safety codes governing the design and use of Kawneer products, such as glazed entrance, window, and curtain wall products, vary widely. Kawneer does not control the selection of product configurations, operating hardware, or glazing materials, and assumes no responsibility therefor.

Kawneer reserves the right to change configuration without prior notice when deemed necessary for product improvement.

© 2015, Kawneer Company, Inc.

GLASSvent® Windows for Storefront Framing

OCTOBER, 2022

PROJECT-OUT WINDOW (1/4" INFILL)

EC 97911-278

Additional information and CAD details are available at www.kawneer.com

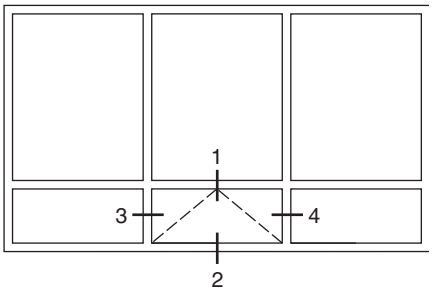

ELEVATION IS NUMBER KEYED TO DETAILS

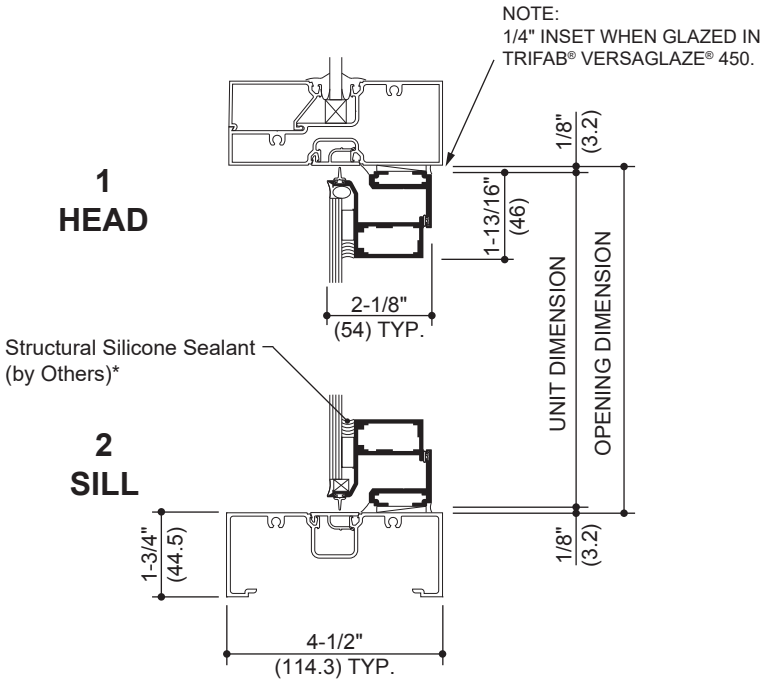

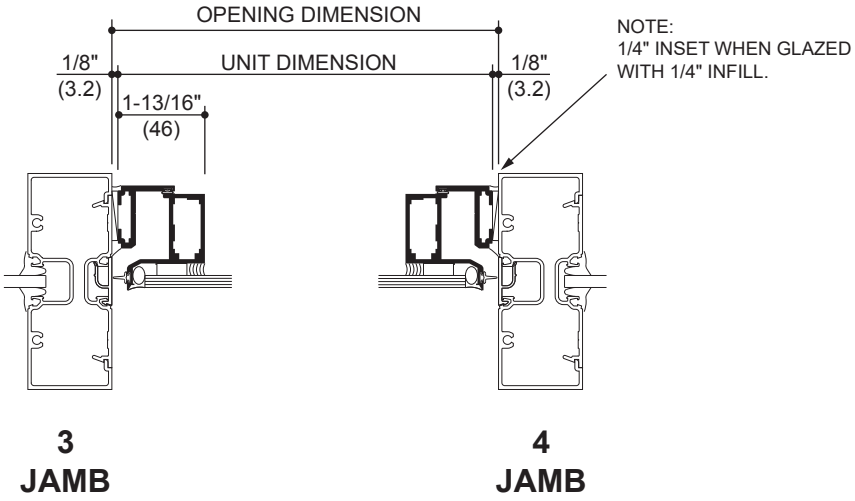

NOTE: THE KAWNEER GLASSvent® WINDOW IS SHOWN IN THESE DETAILS WITH TRIFAB® VERSAGLAZE® 451T STOREFRONT FRAMING FOR REFERENCE. OTHER KAWNEER SYSTEMS CAN BE USED. FOR PRODUCT SPECIFIC APPLICATIONS CONSULT YOUR KAWNEER REPRESENTATIVE.

*** INSTALLER NOTE:** Installer is responsible for all required compatibility review and approvals with the Structural Silicone Manufacturer and the Insulating Glass Unit Manufacturer.

Laws and building and safety codes governing the design and use of Kawneer products, such as glazed entrance, window, and curtain wall products, vary widely. Kawneer does not control the selection of product configurations, operating hardware, or glazing materials, and assumes no responsibility therefor.

Kawneer reserves the right to change configuration without prior notice when deemed necessary for product improvement.

© 2015, Kawneer Company, Inc.

STAINLESS STEEL 4 BAR HINGES	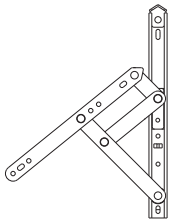	A standard hinge for ventilators providing approximately 45° to 60° openings depending on size. An optional limit stop is available to restrict hinge travel and limit vent opening. Verify with application engineering project specific limit stop requirements based on window size.
CAM HANDLE	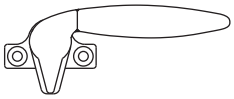	Cast white bronze cam handles are standard for the manual operation and locking of ventilators.
CAM HANDLE WITH POLE RING	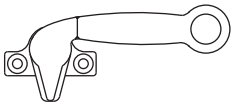	Cast white bronze cam handles with pole ring provide manual operation of ventilators located above reach. These handles are operated with a sash pole.
POLE RING		Cast white bronze pole ring is used in conjunction with locking hardware for sash pole operation of ventilators.
SASH POLE **HANGER FOR SASH POLE**	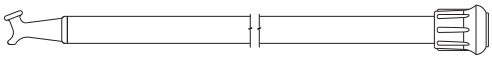 	A 3/4" diameter aluminum sash pole with a cast white bronze pull down hook and black rubber tip. Available in 6 ft. and 12 ft. lengths with optional cast white bronze Pole Hanger.
ACCESS CONTROL LOCK	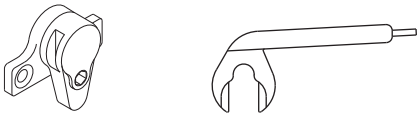	In lieu of cam handles cast white bronze access control locks are offered for managed control of vent operations. Lock is operated with a manganese bronze removable handle.
PIVOT-SHOE ROTO-OPERATOR	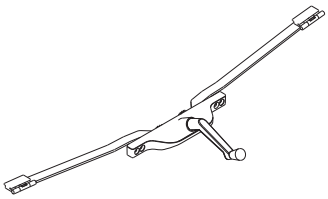	Optional pivot shoe roto operator is located on the center line of the bottom horizontal frame. Standard finish shall be brushed copper nickel to match US-25-D
HOOK BOLT LOCK		For use with pivot-shoe roto operator in lieu of cam handles. Standard finish shall be US-25-D clear white bronze.

Laws and building and safety codes governing the design and use of Kawneer products, such as glazed entrance, window, and curtain wall products, vary widely, Kawneer does not control the selection of product configurations, operating hardware, or glazing materials, and assumes no responsibility therefor.

Kawneer reserves the right to change configuration without prior notice when deemed necessary for product improvement.

© 2015, Kawneer Company, Inc.

CONCEALED LOCK

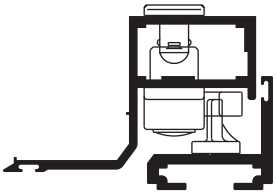

In lieu of cam handles cast white bronze concealed locks are offered for managed control of vent operations. Lock is operated with a removable key.

Laws and building and safety codes governing the design and use of Kawneer products, such as glazed entrance, window, and curtain wall products, vary widely. Kawneer does not control the selection of product configurations, operating hardware, or glazing materials, and assumes no responsibility therefor.

Kawneer reserves the right to change configuration without prior notice when deemed necessary for product improvement.

© 2015, Kawneer Company, Inc.

Product Data Sheet

SOLARBAN® 70
Solar Control Low-E Glass

Aesthetic Description

Solarban® 70 glass (formerly *Solarban*® 70XL glass) is a solar control, low-e glass that brilliantly combines the clear appearance of transparent, color-neutral glass with an exceptional combination of solar control and visible light transmittance (VLT).

The world's first triple-silver, magnetron sputter vacuum deposition (MSVD) coating, *Solarban*® 70 glass expands the design possibilities for buildings in two important ways. First, *Solarban*® 70 glass enables architects to incorporate vast areas of vision glass into their designs without a corresponding increase in cooling equipment capacity.

Second, architects can specify a clear aesthetic while achieving solar control performance that was once attainable only through the use of tinted glass and a solar control, low-e coating in an insulated glass unit (IGU).

Performance Options

When coupled with conventional clear glass in a one-inch IGU, *Solarban*® 70 glass achieves a Visible Light Transmittance (VLT of 64 percent and a Solar Heat Gain Coefficient (SHGC) of 0.27 to produce a Light to Solar Gain (LSG) ratio of 2.37, making it one of the industry's highest-performing glasses.

The clear aesthetic of *Solarban*® 70 glass also makes the product exceptionally versatile, offering architects an extensive array of performance and appearance options. For instance, for projects that require advanced solar control performance, *Solarban*® 70 glass can be coated on the second (#2) surface of nearly all of Vitro Architectural Glass' (formerly PPG glass) wide range of tinted glasses to produce SHGCs as low as 0.19 and LSG ratios ranging from 1.68 to 2.15.

For more color and reflectivity choices, *Solarban*® 70 glass may be specified on the third (#3) surface of an IGU behind a tinted lite or in combination with *Solarcool*® reflective or *Vistacool*® subtly reflective color-enhanced glasses.

The Cirque
Location: Dallas, TX | Product: *Solarban*® 70XL Glass | Architect of Record: PageSoutherlandPage | Design Architect: Gromatzky Dupree & Associates | Glass Fabricator: Trulite Glass and Aluminum Solutions | Glazing Contractor: Haley-Greer

Supporting Sustainable Design

Vitro Architectural Glass provides abundant opportunities for architects and building owners to realize their sustainability objectives.

Energy Use & Operating Cost Reduction: High-performance glasses by Vitro are engineered to facilitate downsized mechanical equipment costs, leading to reduced long-term energy costs. Visit **tools.vitroglazings.com** for glass comparison and configuration tools for analyzing glass products.

Sustainability Documentation: Vitro Architectural Glass is the first U.S. float glass manufacturer to have its entire selection of products recognized by the *Cradle to Cradle Certified*™ program, and the first in North America to publish third-party verified Environmental Product Declarations (EPDs) for its Flat Glass and Processed Glass products.

For additional credit opportunities and supporting documentation, visit **vitroglazings.com/LEED**

LEED® Credit Opportunities

Possible Points	LEED Credit	*Solarban*® 70 Feature	Path/Option Satisfied
18	**Energy & Atmosphere (EA)** Optimize Energy Performance	Excellent SHGC, U-value and Tvis performance	Whole Building Energy Simulation (Option 1) or Prescriptive Compliance: ASHRAE Advanced Energy Design Guide (Option 2)
5	**Innovation (IN)** Innovation in Design	Exceeds minimum performance mandated by local energy codes	Innovation (Option 1), Pilot (Option 2) and Exemplary Performance (Option 3)
3	**Indoor Environmental Quality (EQ)** Daylight	Exhibits high light transmission	Simulation: Spatial Daylight Autonomy and Annual Sunlight Exposure (Option 1), Simulation: Illuminance Calculations (Option 2) or Measurement (Option 3)

Solarban® 70 Glass

Insulating Glass Unit Performance Comparisons | 1-inch (25mm) units with 1/2-inch (13mm) airspace and two 1/4-inch (6mm) lites							
Glass Type: Outdoor Lite: Coating if Any (Surface) Glass + Indoor Lite: Coating if Any (Surface) Glass	Visible Light Transmittance (VLT) %	Visible Light Reflectance		(BTU/hr°ft²°°F) NFRC U-Value		Solar Heat Gain Coefficient (SHGC)	Light to Solar Gain (LSG)
		Exterior %	Interior %	Winter Nighttime	Winter Argon		
***Solarban*® 70 Solar Control Low-E Glass**							
Solarban® 70 (2) + Clear	64	13	14	0.28	0.24	0.27	2.37
Solarban® 70 (2) *Solexia*® + Clear	56	11	14	0.28	0.24	0.26	2.15
Solarban® 70 (2) *Atlantica*® + Clear	49	10	13	0.28	0.24	0.23	2.13
Solarban® 70 (2) *Azuria*® + Clear	50	10	13	0.28	0.24	0.24	2.08
Solarban® 70 (2) *Solarblue*® + Clear	41	8	13	0.28	0.24	0.22	1.86
Solarban® 70 (2) *Pacifica*® + Clear	31	7	13	0.28	0.24	0.19	1.63
Solarban® 70 (2) *Solarbronze*® + Clear	39	8	13	0.28	0.24	0.20	1.95
Solarban® 70 (2) *Optigray*® + Clear	46	9	13	0.28	0.24	0.23	2.00
Solarban® 70 (2) *Solargray*® + Clear	32	7	13	0.28	0.24	0.19	1.68
Solexia® + *Solarban*® 70 (3) Clear	56	11	12	0.28	0.24	0.32	1.75
Atlantica® + *Solarban*® 70 (3) Clear	48	9	11	0.28	0.24	0.28	1.71
Azuria® + *Solarban*® 70 (3) Clear	49	9	11	0.28	0.24	0.29	1.69
Solarblue® + *Solarban*® 70 (3) Clear	41	8	12	0.28	0.24	0.27	1.52
Pacifica® + *Solarban*® 70 (3) Clear	31	6	10	0.28	0.24	0.22	1.41
Solarbronze® + *Solarban*® 70 (3) Clear	38	8	11	0.28	0.24	0.26	1.46
Optigray® + *Solarban*® 70 (3) Clear	46	9	12	0.28	0.24	0.28	1.64
Solargray® + *Solarban*® 70 (3) Clear	32	7	11	0.28	0.24	0.24	1.33
Graylite® II + *Solarban*® 70 (3) Clear	6	4	10	0.28	0.24	0.11	0.55
Vistacool*® and *Solarcool*® with *Solarban*® 70 Solar Control Low-E (3)							
Vistacool® (2) *Azuria*® + *Solarban*® 70 (3)	38	21	23	0.28	0.24	0.24	1.58
Vistacool® (2) *Pacifica*® + *Solarban*® 70 (3)	24	11	22	0.28	0.24	0.19	1.26
Solarcool® (2) *Azuria*® + *Solarban*® 70 (3)	19	19	27	0.28	0.24	0.16	1.19
Solarcool®(2) *Solarblue*® + *Solarban*® 70 (3)	16	14	28	0.28	0.24	0.15	1.07
Solarcool®(2) *Pacifica*® + *Solarban*® 70 (3)	12	10	27	0.28	0.24	0.13	0.92
Solarcool®(2) *Solarbronze*® + *Solarban*® 70 (3)	15	14	27	0.28	0.24	0.15	1.00
Solarcool®(2) *Solargray*® + *Solarban*® 70 (3)	13	11	27	0.28	0.24	0.14	0.93

**Solarban*® 70 glass for annealed applications is applied to *Starphire*® glass, heat treated applications will require either clear or *Starphire*® glass depending on manufacturing process.

All performance data calculated using LBNL Window 7.3 software and represents center of glass performance data. For detailed information on the methodologies used to calculate the aesthetic and performance values in this table, please visit vitroglazings.com or request our Architectural Glass Catalog.

Fabrication and Availability

Solarban® 70 glass is available exclusively through the *Vitro Certified*™ Network. *Vitro Certified*™ Fabricators can meet tight construction deadlines and accelerate the delivery of replacement glass before, during and after construction. *Solarban*® 70 glass is manufactured using the sputter-coating process and is available for annealed, heat-strengthened and tempered applications.

Additional Resources

To obtain samples of any Vitro Glass product, call **1-855-VTRO-GLS (877-6457)** or visit **samples.vitroglazings.com**. For videos, design insights and technical education, visit the Vitro Glass Education Center at **glassed.vitroglazings.com**. For glass comparison and configuration tools, visit **tools.vitroglazings.com.**

For more information about *Solarban*® low-e glass and other *Cradle to Cradle Certified*™ architectural glasses by Vitro Glass, visit **vitroglazings.com**, or call **1-855-VTRO-GLS (887-6457).**

©2022 Vitro Architectural Glass. All rights reserved. *Atlantica*®, *Azuria*®, *Graylite*®, *Optigray*®, *Pacifica*®, *Solarban*®, the *Solarban*® logo, *Solarblue*®, *Solarbronze*®, *Solarcool*®, *Solargray*®, *Solexia*®, *Starphire*® and *Vistacool*® are registered trademarks owned by Vitro. *Vitro Certified*™ is a trademark owned by Vitro. *Cradle to Cradle Certified*™ is a trademark licensed by the Cradle to Cradle Products Innovation Institute. LEED® —an acronym for Leadership in Energy and Environmental Design—is a registered trademark of the U.S. Green Building Council. Printed in the USA. 7097 (04/22)

CERTIFIED cradletocradle

Vitro® Architectural Glass